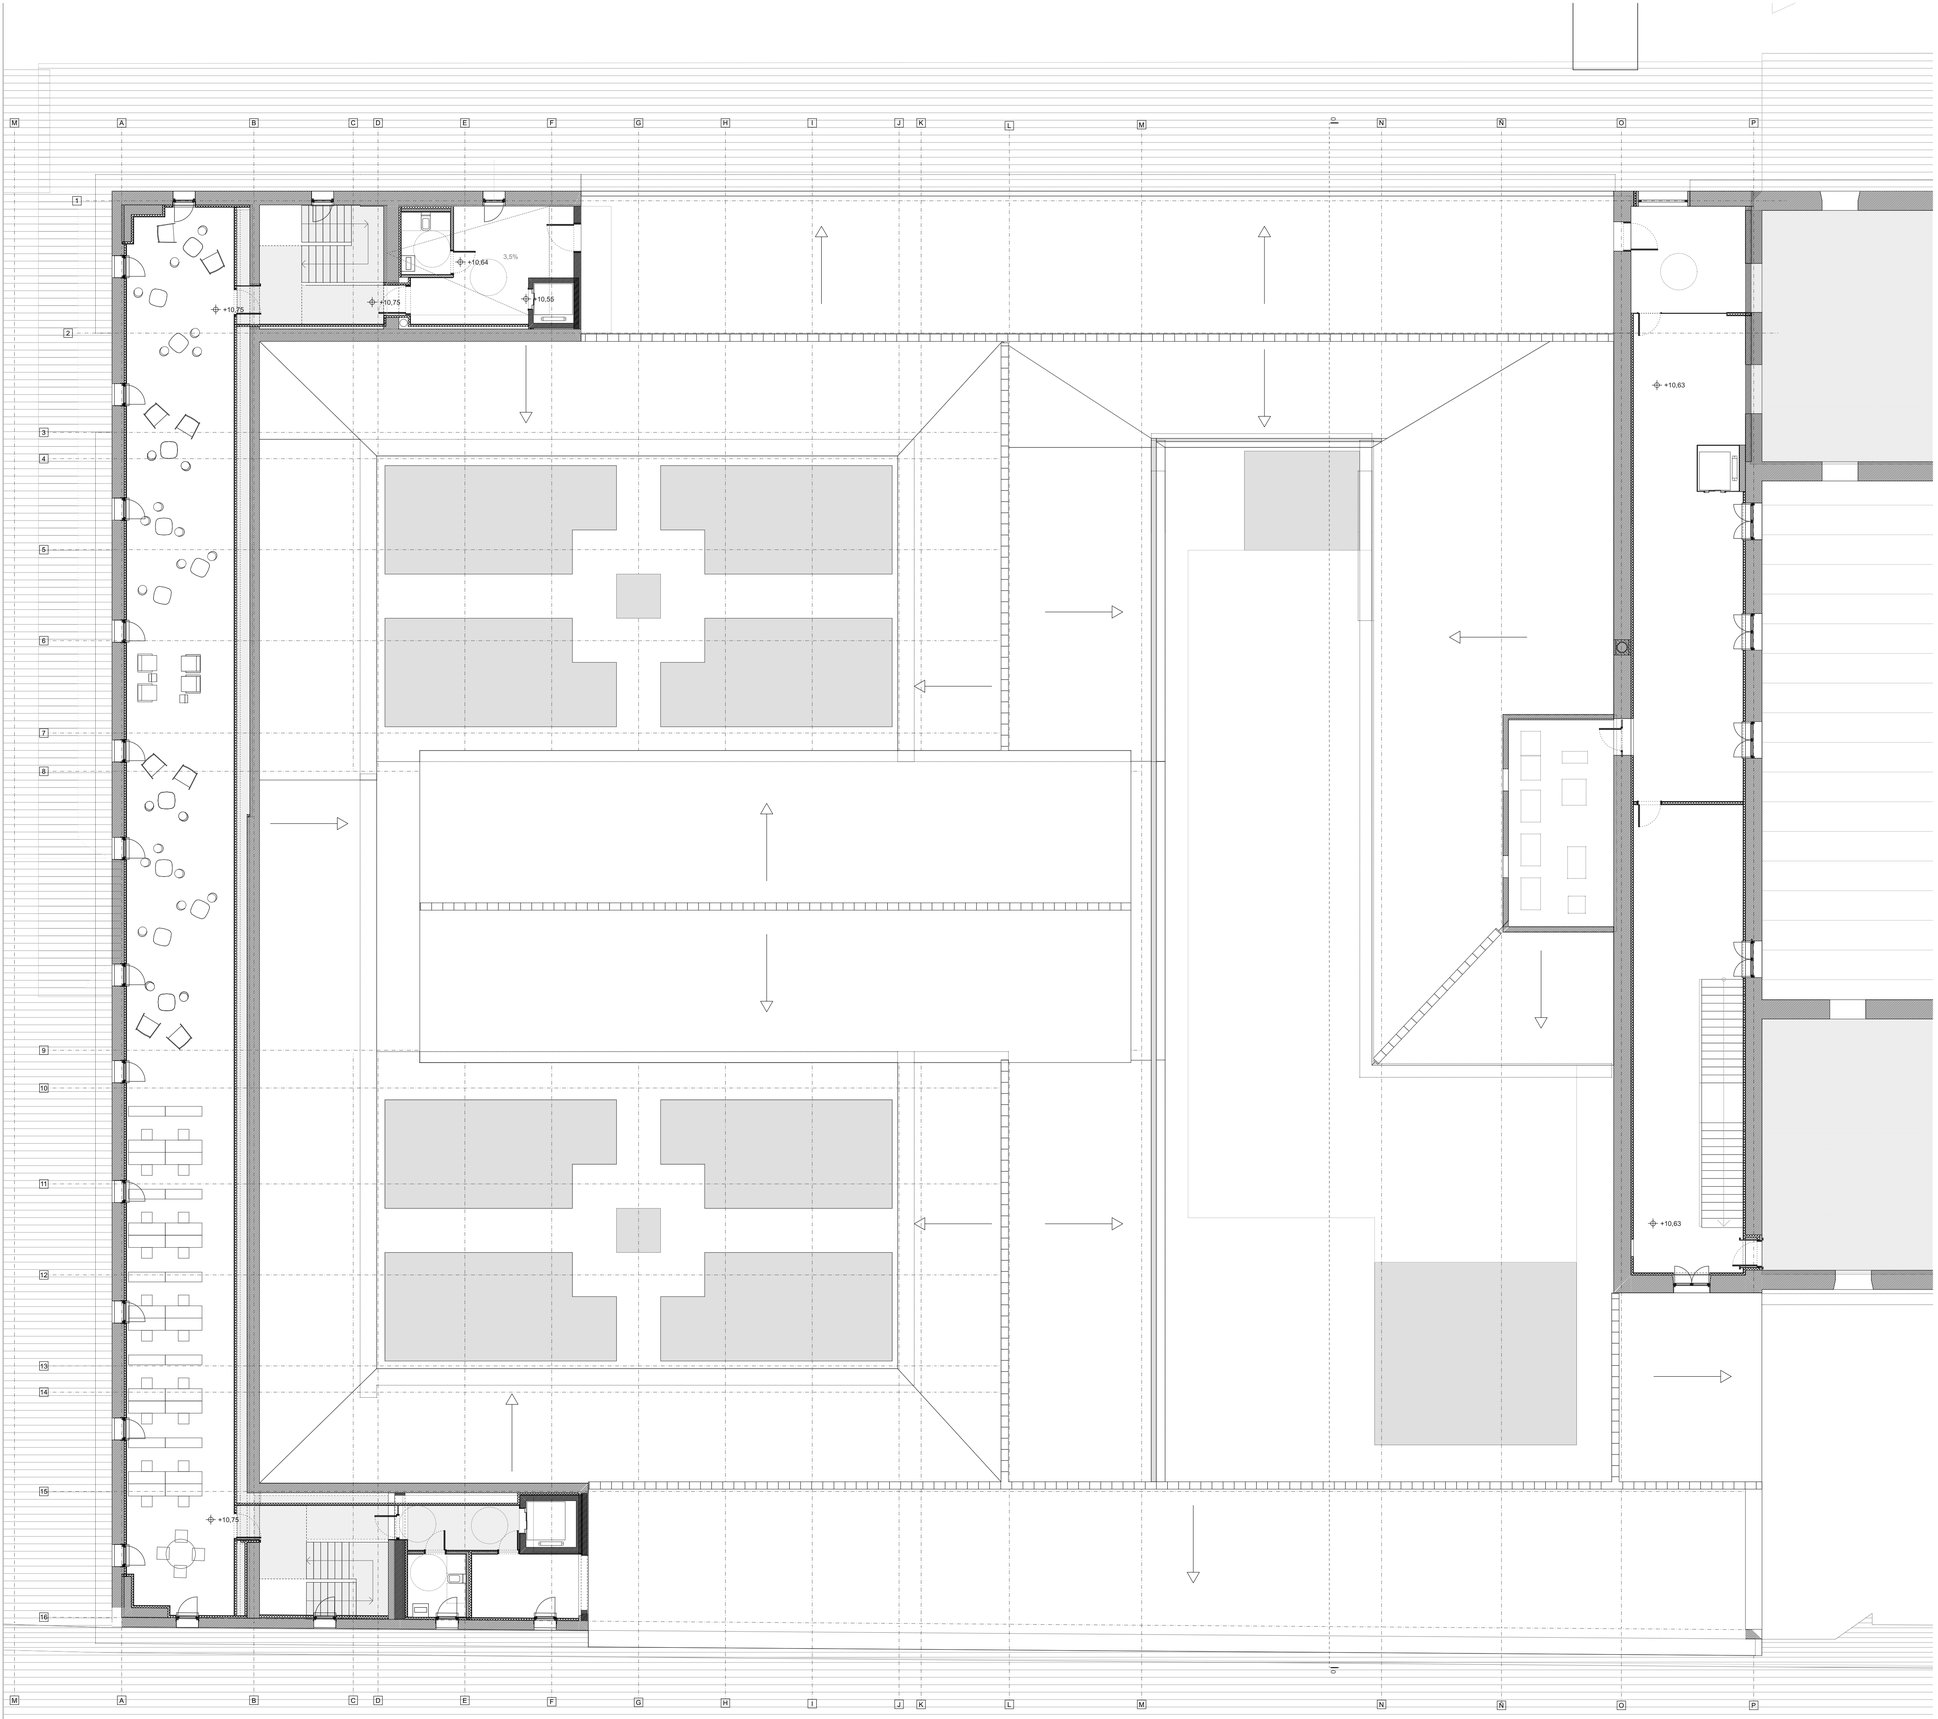



NOTAS GENERALES

No tomar medidas sobre planos.
Todas las dimensiones se deben comprobar en obra.
Todas las dimensiones están referenciadas a las divisiones sin tener en cuenta los acabados.
Posibles contradicciones entre documentos del proyecto deben ser comunicadas inmedia- tamente a la D.F. que determinará su validez y prioridad.
Los planos deben ser leidos en conjunto con todos los documentos relevantes del proyecto, incluida la documentación escrita y los planos de estructuras, instalaciones y fachada.
Consultar los pliegos de condiciones antes de la puesta en obra.
No válido para construir sin la firma de aprobación de la D.F.
Prohibida la reproducción o difusión total o parcial de cualquier documento del proyecto sin la autorización expresa de la D.F.
Las bases informáticas de los documentos del proyecto son propiedad intelectual de los autores. Prohibida su reproducción o difusión.

MODIFICACIONES

© Copyright 2018. Ramón Esteve Estudio de Arquitectura. Valencia.

EQUIPO REDACTOR

ARQUITECTURA

**UTE RE_ICR**

RAMÓN ESTEVE ESTUDIO DE ARQUITECTURA, S.L.P.
CIRO MANUEL VIDAL CLIMENT
IVO ELISEO VIDAL CLIMENT

REPRESENTANTE:

RAMON ESTEVE CAMBRA
RAMON ESTEVE ESTUDIO DE ARQUITECTURA SLP

PLAÇA PERE BORRESCO I GALINDO 7 1º
46003 VALENCIA. TEL 96 351 04 34
FAX 96 315 55 34
www.ramonesteve.com

PROMOTOR

AJUNTAMENT D'ALACANT
AYUNTAMIENTO DE ALICANTE

PLAZA DEL AYUNTAMIENTO Nº1
03002 ALICANTE
ALICANTE



FASE

FINAL DE OBRA

FIRMADO

UTE RE _CIVI
REPRESENTANTE UTE
RAMON ESTEVE CAMBRA
ARQUITECTO

UBICACIÓN DEL PROYECTO

CONJUNTO ARQUITECTÓNICO "LAS CIGARRERAS"
CALLE SEVILLA Nº2
03012 ALICANTE (ALICANTE)

PROYECTO

REHABILITACIÓN DE LA FASE I
"ANTIGUA CASA DE MISERICORDIA"

Nº REVISION
00


Nº PLANO
03.1.3

FECHA
MARZO 2026

ESCALA
1:1000, 1:125
(FORMATO A3) ESC: 1/250

PLANO PLANTAS DE DISTRIBUCIÓN

DISTRIBUCIÓN PLANTA SEGUNDA

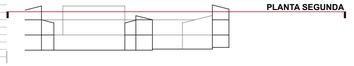


RE_ ICR